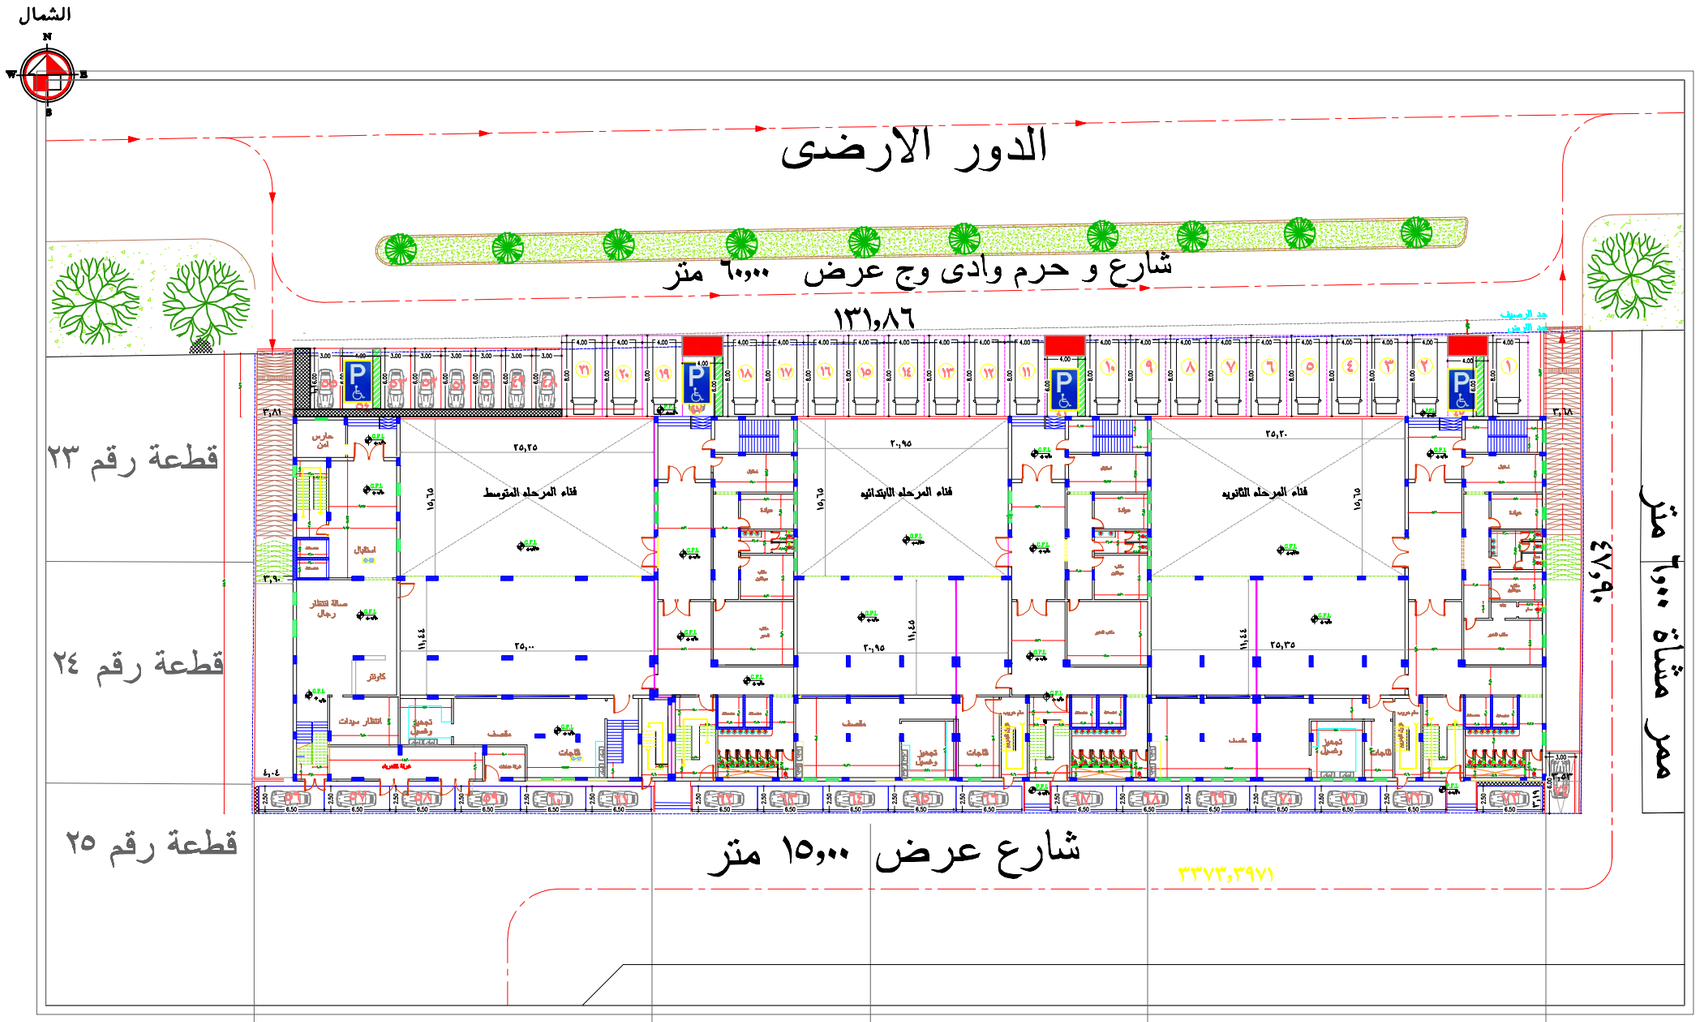

المملكة العربية السعودية

مكتب الغوص للاستشارات الهندسيه

الطـــائف – ت ٧٤٩٤٧٤٤

بيانات الموقع

المنطقة	مكة المكرمة		عدد الادوار المسموحه	دور ارضى +ثلاث ادوار
الموقع	الطائف	الحى الجفيجف	وصف المبنى	مجمع مدارس
رقم القطعة	١١-١٢-١٣-١٤-١٥-١٦ ١٧-١٨-١٩-٢٠-٢١-٢٢		رقم المخطط	١٣٤٨

بيانات المشروع

مساحة الارض	٦١٦٤,٠٩ م٢
عدد الادوار	(٤) ادوار وقبو
وصف المبنى	مجمع مدارس ابتدائى و متوسط وثانوى مكون من (٤) ادوار وقبو
نسبة البناء (الدو الارضى)	٥٤,٧٢٪
مساحة الدور الارضى	٣٣٧٣,٤٠ م٢

الدور	الارض	المبنى	النسبة	المنسوب
القبو	٦١٦٤,٠٩ م٢	٢٩٩٣,١٢	٤٨,٥٥ ٪	-٣,٠٠ م
الارضى		٣٣٧٣,٤٠ م٢	٥٤,٧٢٪	+ ١,٢٠ م
الاول		٣٤٠٣,٠٩ م٢	٥٥,٢٠ ٪	+٤,٨٠م
الثانى		٣٤٠٣,٠٩ م٢	٥٥,٢٠ ٪	+٨,٤٠م
الثالث		٣٤٠٣,٠٩ م٢	٥٥,٢٠ ٪	+١٢,٠٠م
بيت الدرج	٣٤٠٣,٠٩ م٢	٣٦٦,٤٠م٢	١,٠٧٦٪	+ ١٥,٦٠ م
غرفة كهرباء		٥٧,٠٠	٠,٩٢٪	القبو والارضى -٣,٠٠ م + ٦,٢٠ م
غرفة خدمات المضخات		٨٩,٠٠ م٢	١,٤٤٪	القبو -٣,٠٠ م

جدول الارتدادات

الدور	شـمال	شـرق	جـنوب	غـرب
الارضـى	٦,٢٩ م	٣,٥٣م	٣,١٩ م	٣,٨١ م

الاسـم	محمد بن أحمد بن معيض الزهرانى
المـوقع	الطائف – حى الجفيجف
اسـم اللوحة	المسقط الافقى للدور الارضى
مقياس الرسم	١ / ١٠٠ — التاريخ

المهندس المعمارى	محمد الهادى السويسى	الدرجه المهنيه	محترف	رقم العضويه	٢١٧٢٩٩	
المهندس المعمارى	سمير على محمود	الدرجه المهنيه	محترف	رقم العضويه	٣٤٧٧١	
المهندس الانشائى	مصطفى محمود	الدرجه المهنيه	مشارك	رقم العضويه	٢٦٣٧٠١	
مهندس الكهرباء	احمد صبيح	الدرجه المهنيه	مهندس	رقم العضويه	٨٨٩٧٧٩	
مهندس الميكانيكا	محمد سيد فهمى	الدرجه المهنيه	مهندس	رقم العضويه	٨٨٦٣٤٣	

مدير المكتب	المهندس/ عبدالرحمن بن حسن بن غوص	الختم
التوقيع	الغوص للاستشارات الهندسية — تصميم . تخطيط . إشراف . استشارات معماريه . إدارة مشاريع . تخطيط مبني وحضري . تقييمات الأراضي العلميه والزراعيه . استشارات جيولوجيه . طرق وكباري . دراسات مياه وصرف صحي	

المرحله الثانويه

خدمات
مقصف
ادارة

المرحله الابتدائيه

خدمات
مقصف
ادارة

المرحله المتوسط

خدمات
مقصف
ادارة

الاداره والمسرح

انتظار
استقبال
ادارة

جدول الاطوال والمساحات

الاستخدام	الطول	المساحة	الاستخدام	المساحة
السور	١٦٥,٠٠ م ط	٣٣٠,٠٠ م٢	بيارة الصرف	ـــ م٢
السترة	٣٠٥,٠٠ م	٦١,٠٠م٢	خزان المياه الارضى	٢٩٦,٧٤ م٢

جدول البروزات

بروز شمالى	١,٦٥ م ط	بروز شرقى	ـــ م ط
بروز جنوبى	ـــ م ط	بروز غربى	ـــ م ط