المملكة العربية السعودية

مكتب الغوص للاستشارات الهندسيه

الطـــائف – ت ٧٤٩٤٧٤٤

شارع و حرم وادى وج عرض ٦٠,٠٠ متر

قطعة رقم ٢٣

قطعة رقم ٢٤

قطعة رقم ٢٥

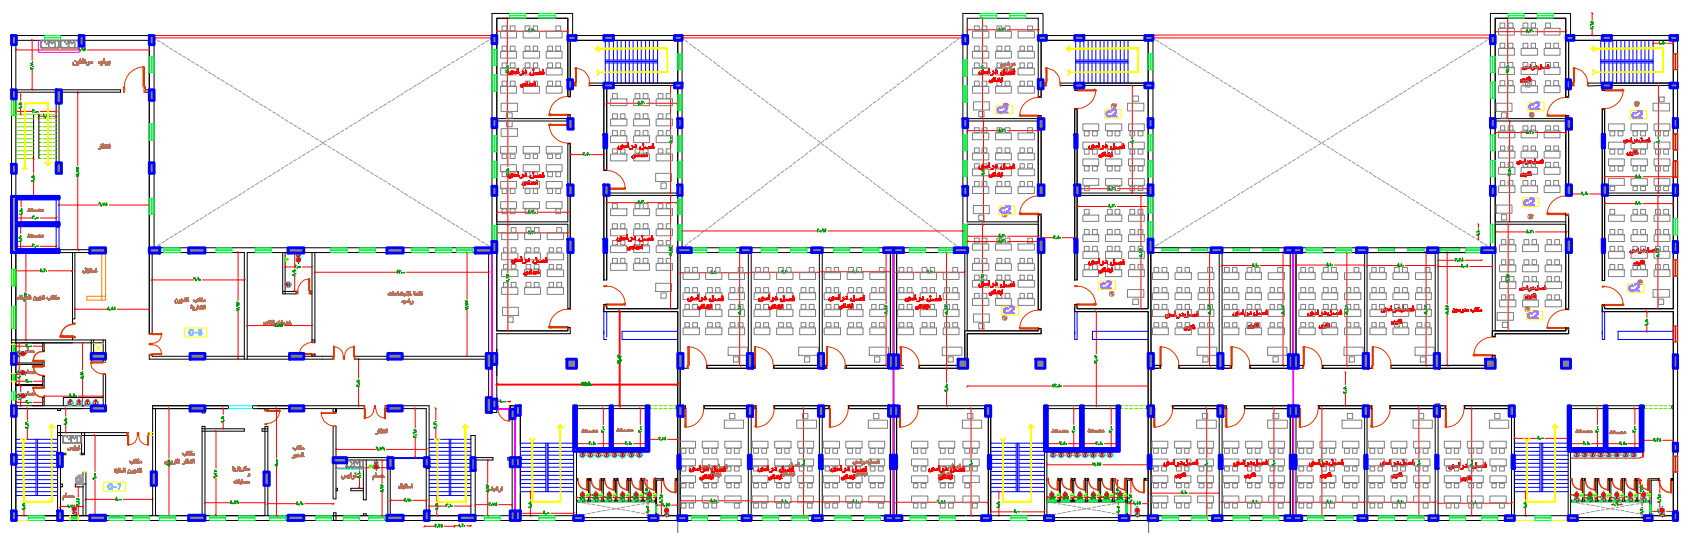

مشاة ٦,٠٠ متر

شارع عرض ١٥,٠٠ متر

المرحله الثانويه

خدمات

فصول ثانوى

المرحله الابتدائيه

خدمات

فصول ابتدائى

المرحله المتوسط

خدمات

فصول متوسط

الاداره والمسرح

خدمات

ادارة

الاســـم	محمد بن أحمد بن معيض الزهرانى
المـــوقع	الجفيجف
اســم اللوحة	المسقط الافقى للدور الاول
مقياس الرسم	١ / ١٠٠
التاريخ	
التوقيع	

المهندس المعمارى	محمد العادى السويسى	الدرجه المهنيه	محترف	رقم العضويه	٢١٧٢٩٩	
المهندس المعمارى	سمير على محمود	الدرجه المهنيه	محترف	رقم العضويه	٣٤٧٧١	
المهندس الانشائى	مصطفى محمود	الدرجه المهنيه	مشارك	رقم العضويه	٢٦٣٧٠١	
مهندس الكهرباء	احمد صبيح	الدرجه المهنيه	مهندس	رقم العضويه	٨٨٩٧٧٩	
مهندس الميكانيكا	محمد سيد فهمى	الدرجه المهنيه	مهندس	رقم العضويه	٨٨٦٣٤٣	

مدير المكتب	المهندس/ عبدالرحمن بن حسن بن غوص	الختم

الغوص للهندسة

تصميم - تخطيط - دراسات - إشراف

مساحة مساحة - دراسات طرق - دراسات تربة